




NOUVELLE RÉSIDENCE
ST-MICHEL DE BELLECHASSE
GUILLAUME PLANTE

POUR SOUMISSION 10/07/2013
POUR INFORMATION 04/06/2013

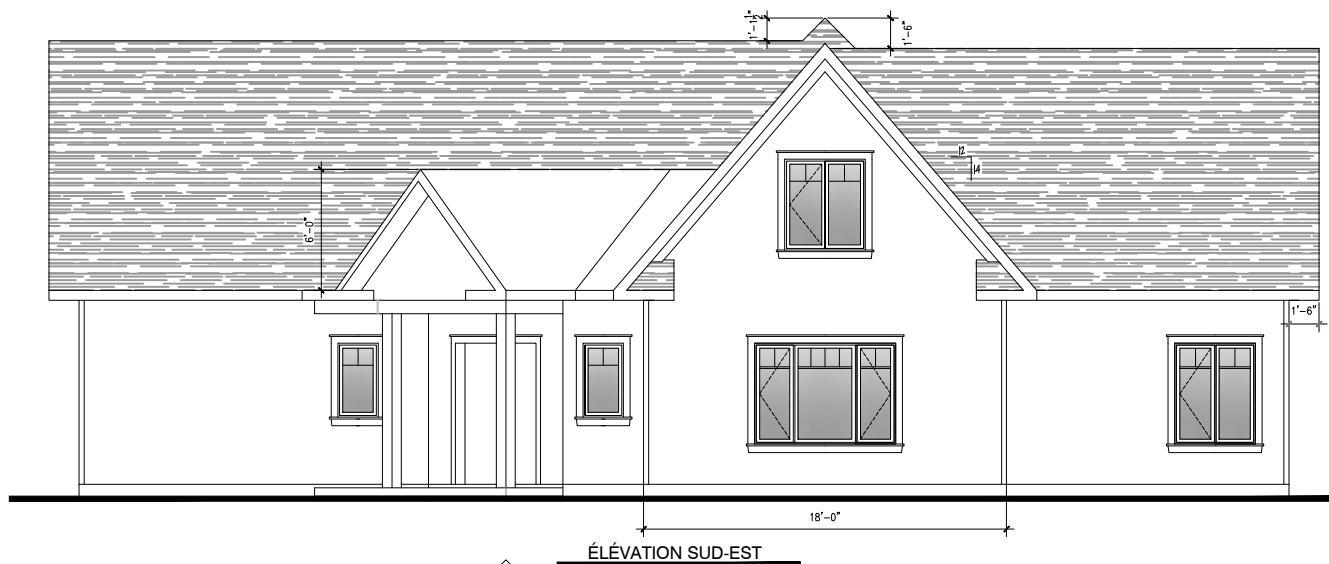

CLIENT
Guillaume Plante
418-261-2190
guillaume.plante@frimastudio.com

PROJET
NOUVELLE
RÉSIDENCE
lot 3 884 373
Chemin de la bouée
St-Michel de Bellechasse



DESSIN
ÉLÉVATIONS

DESSINÉ PAR
JÉRÔME ROY

DATE
04/06/2013

ECHELLE
1/4" = 1'-0"

FEUILLE
1/6

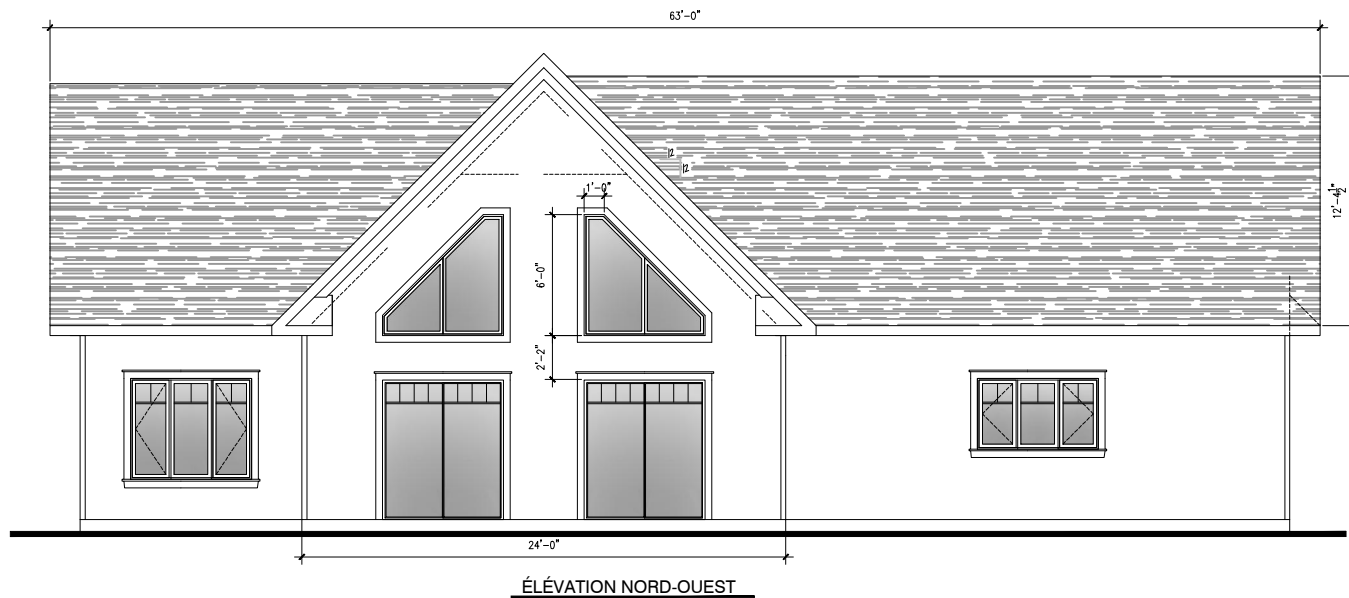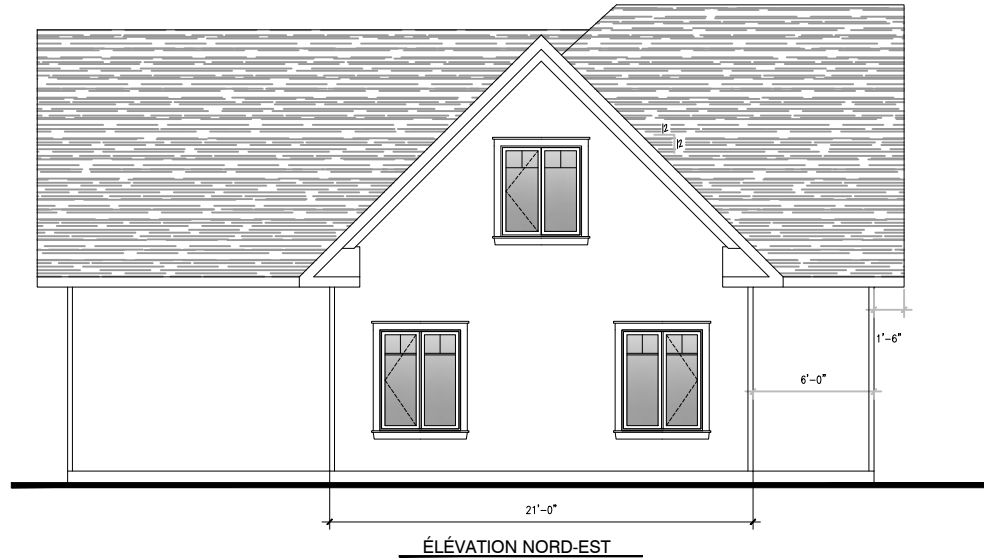

NOUVELLE RÉSIDENCE
ST-MICHEL DE BELLECHASSE
GUILLAUME PLANTE

POUR SOUMISSION 10/07/2013
POUR INFORMATION 04/06/2013




CLIENT
Guillaume Plante
418-261-2190
guillaume.plante@frimastudio.com

PROJET
NOUVELLE
RÉSIDENCE
lot 3 884 373
Chemin de la bouée
St-Michel de Bellechasse

DESSIN
ÉLEVATIONS

DESSINÉ PAR
JÉRÔME ROY
ECHELLE
1/4" = 1'-0"

DATE
04/06/2013
FEUILLE
2/6

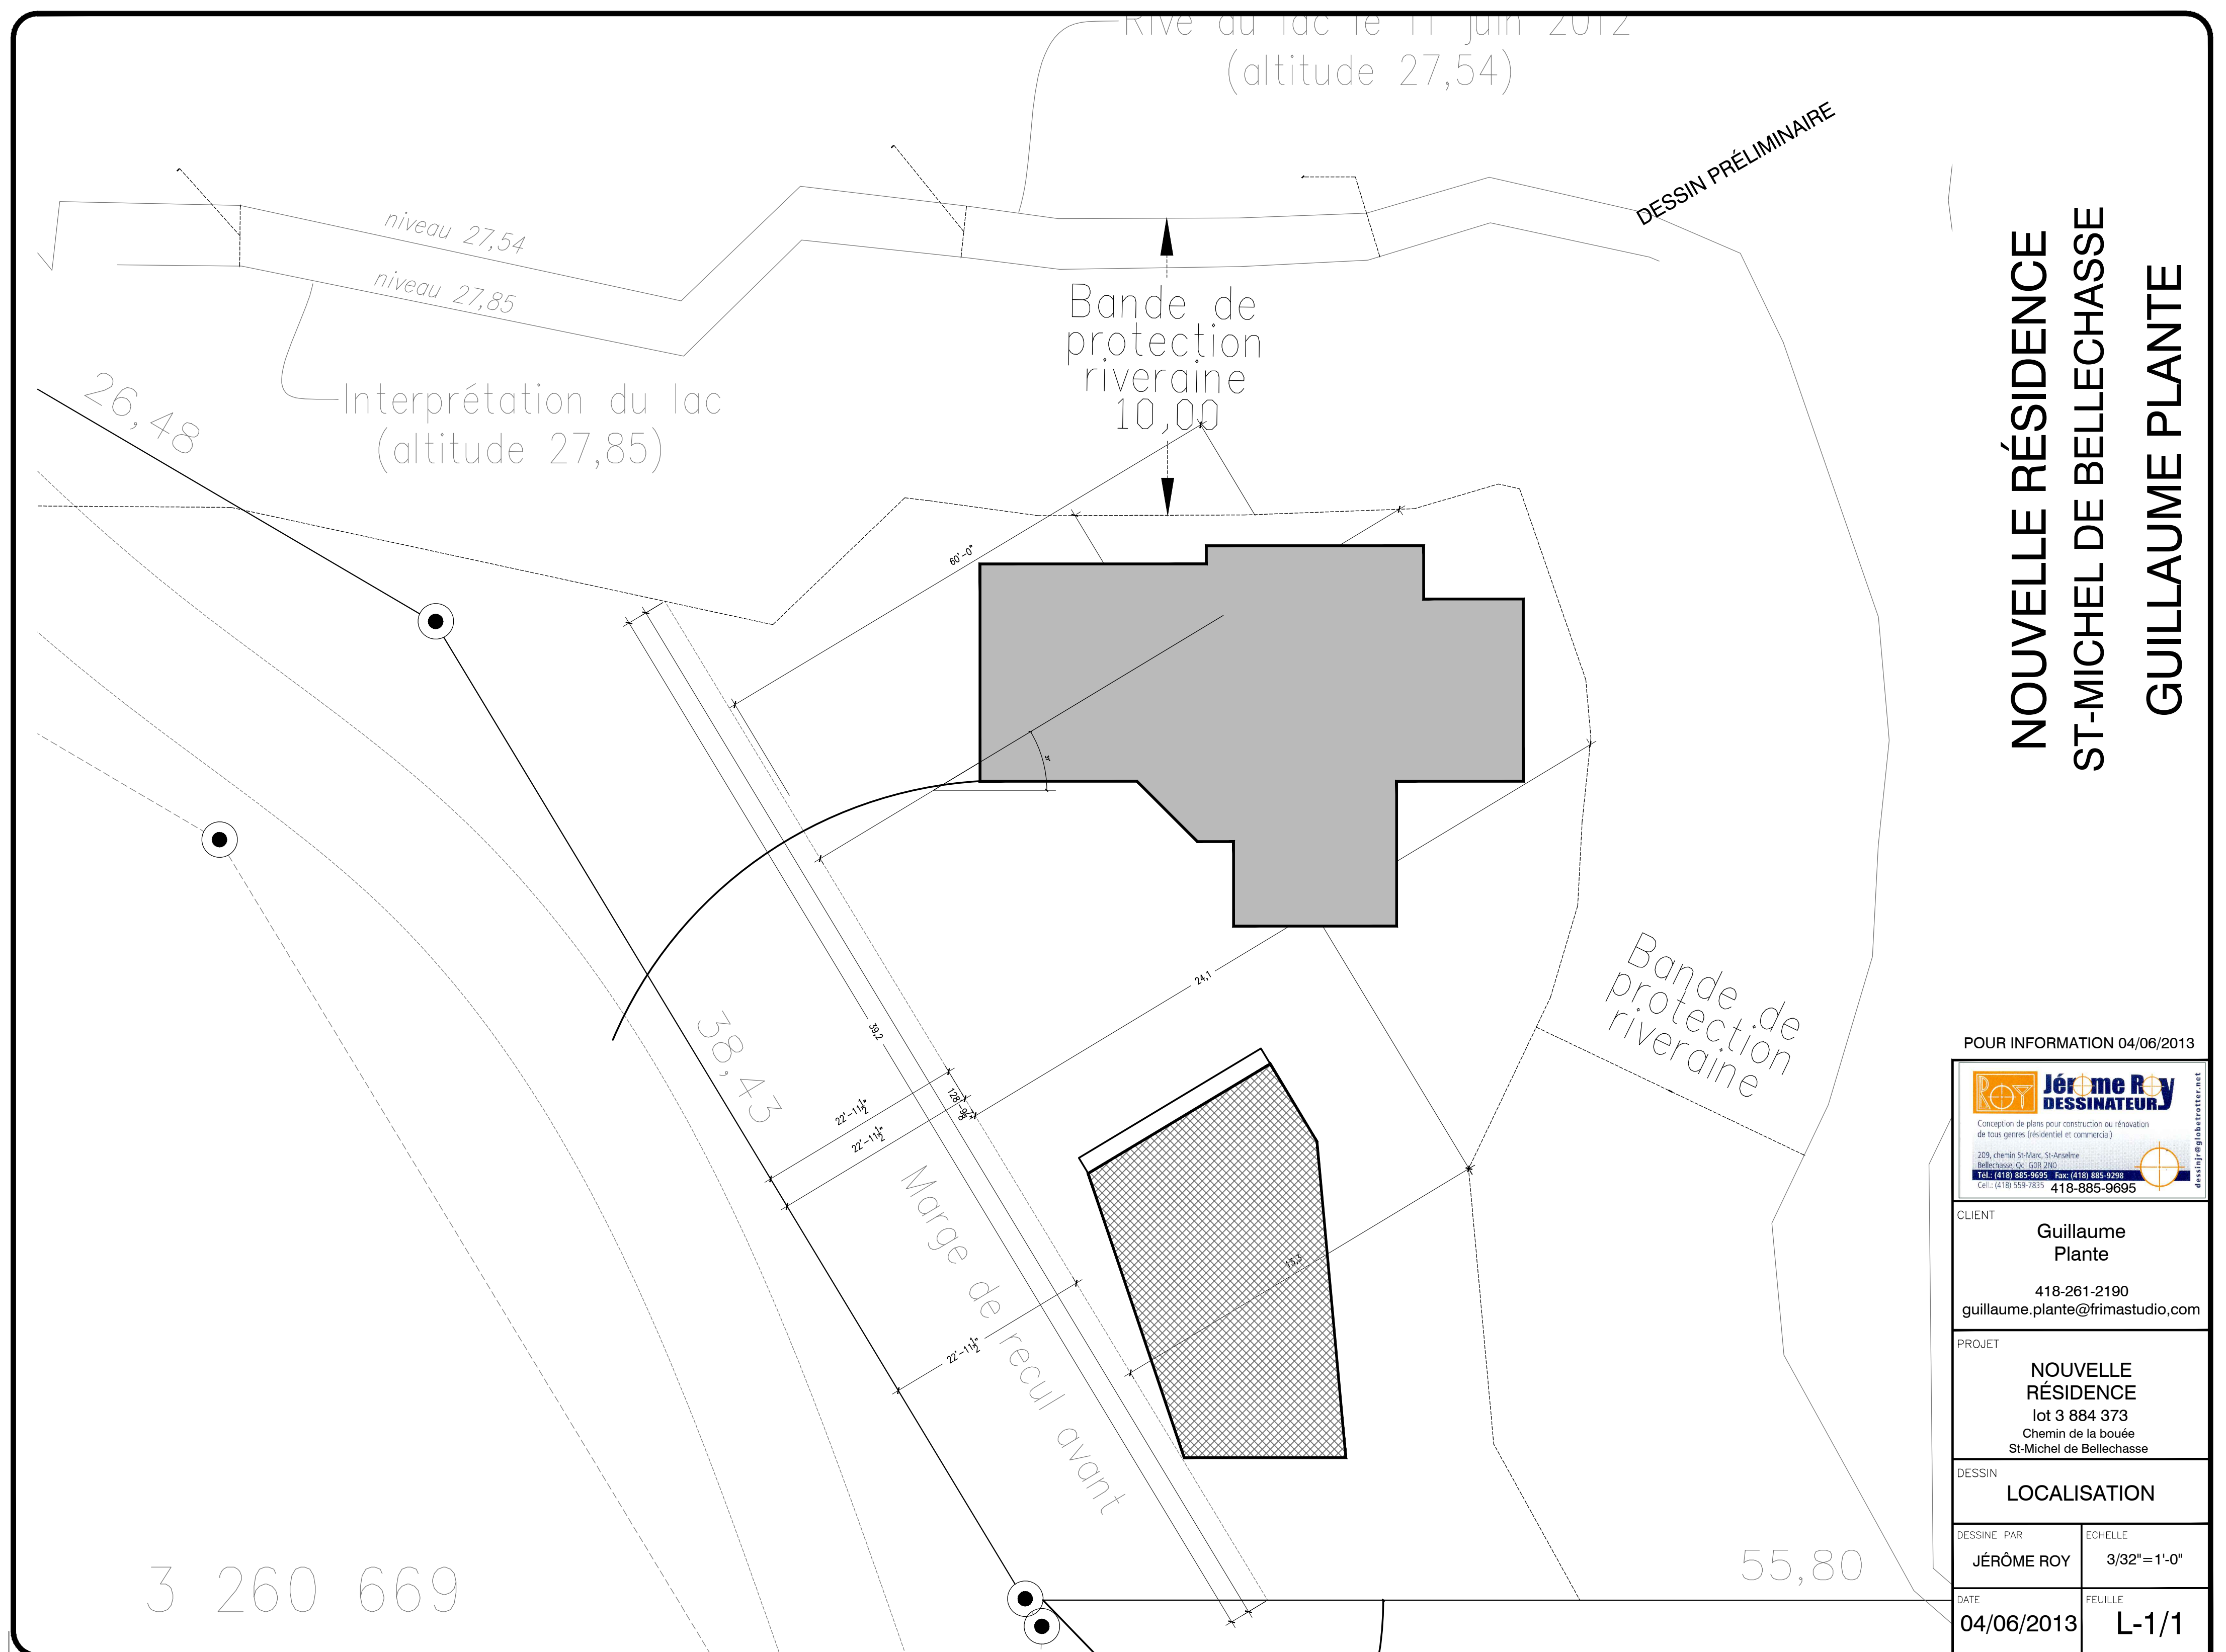

NOUVELLE RÉSIDENCE
ST-MICHEL DE BELLECHASSE
GUILLAUME PLANTE

POUR INFORMATION 04/06/2013



Jérôme Roy
DESSINATEUR

Conception de plans pour construction ou rénovation
de tous genres (résidentiel et commercial)

209, chemin St-Marc, St-Anselme
Bellechasse, Qc G0B 2V0
Tel.: (418) 885-9695 Fax: (418) 885-9298
Cell.: (418) 939-7839 418-885-9695



dessin@glebetrotter.net

CLIENT

Guillaume Plante

418-261-2190
guillaume.plante@frimastudio.com

PROJET

**NOUVELLE
RÉSIDENCE**
lot 3 884 373
Chemin de la bouée
St-Michel de Bellechasse

DESSIN

LOCALISATION

DESSINÉ PAR	ECHELLE
JÉRÔME ROY	3/32"=1'-0"

DATE	FEUILLE
04/06/2013	L-1/1